


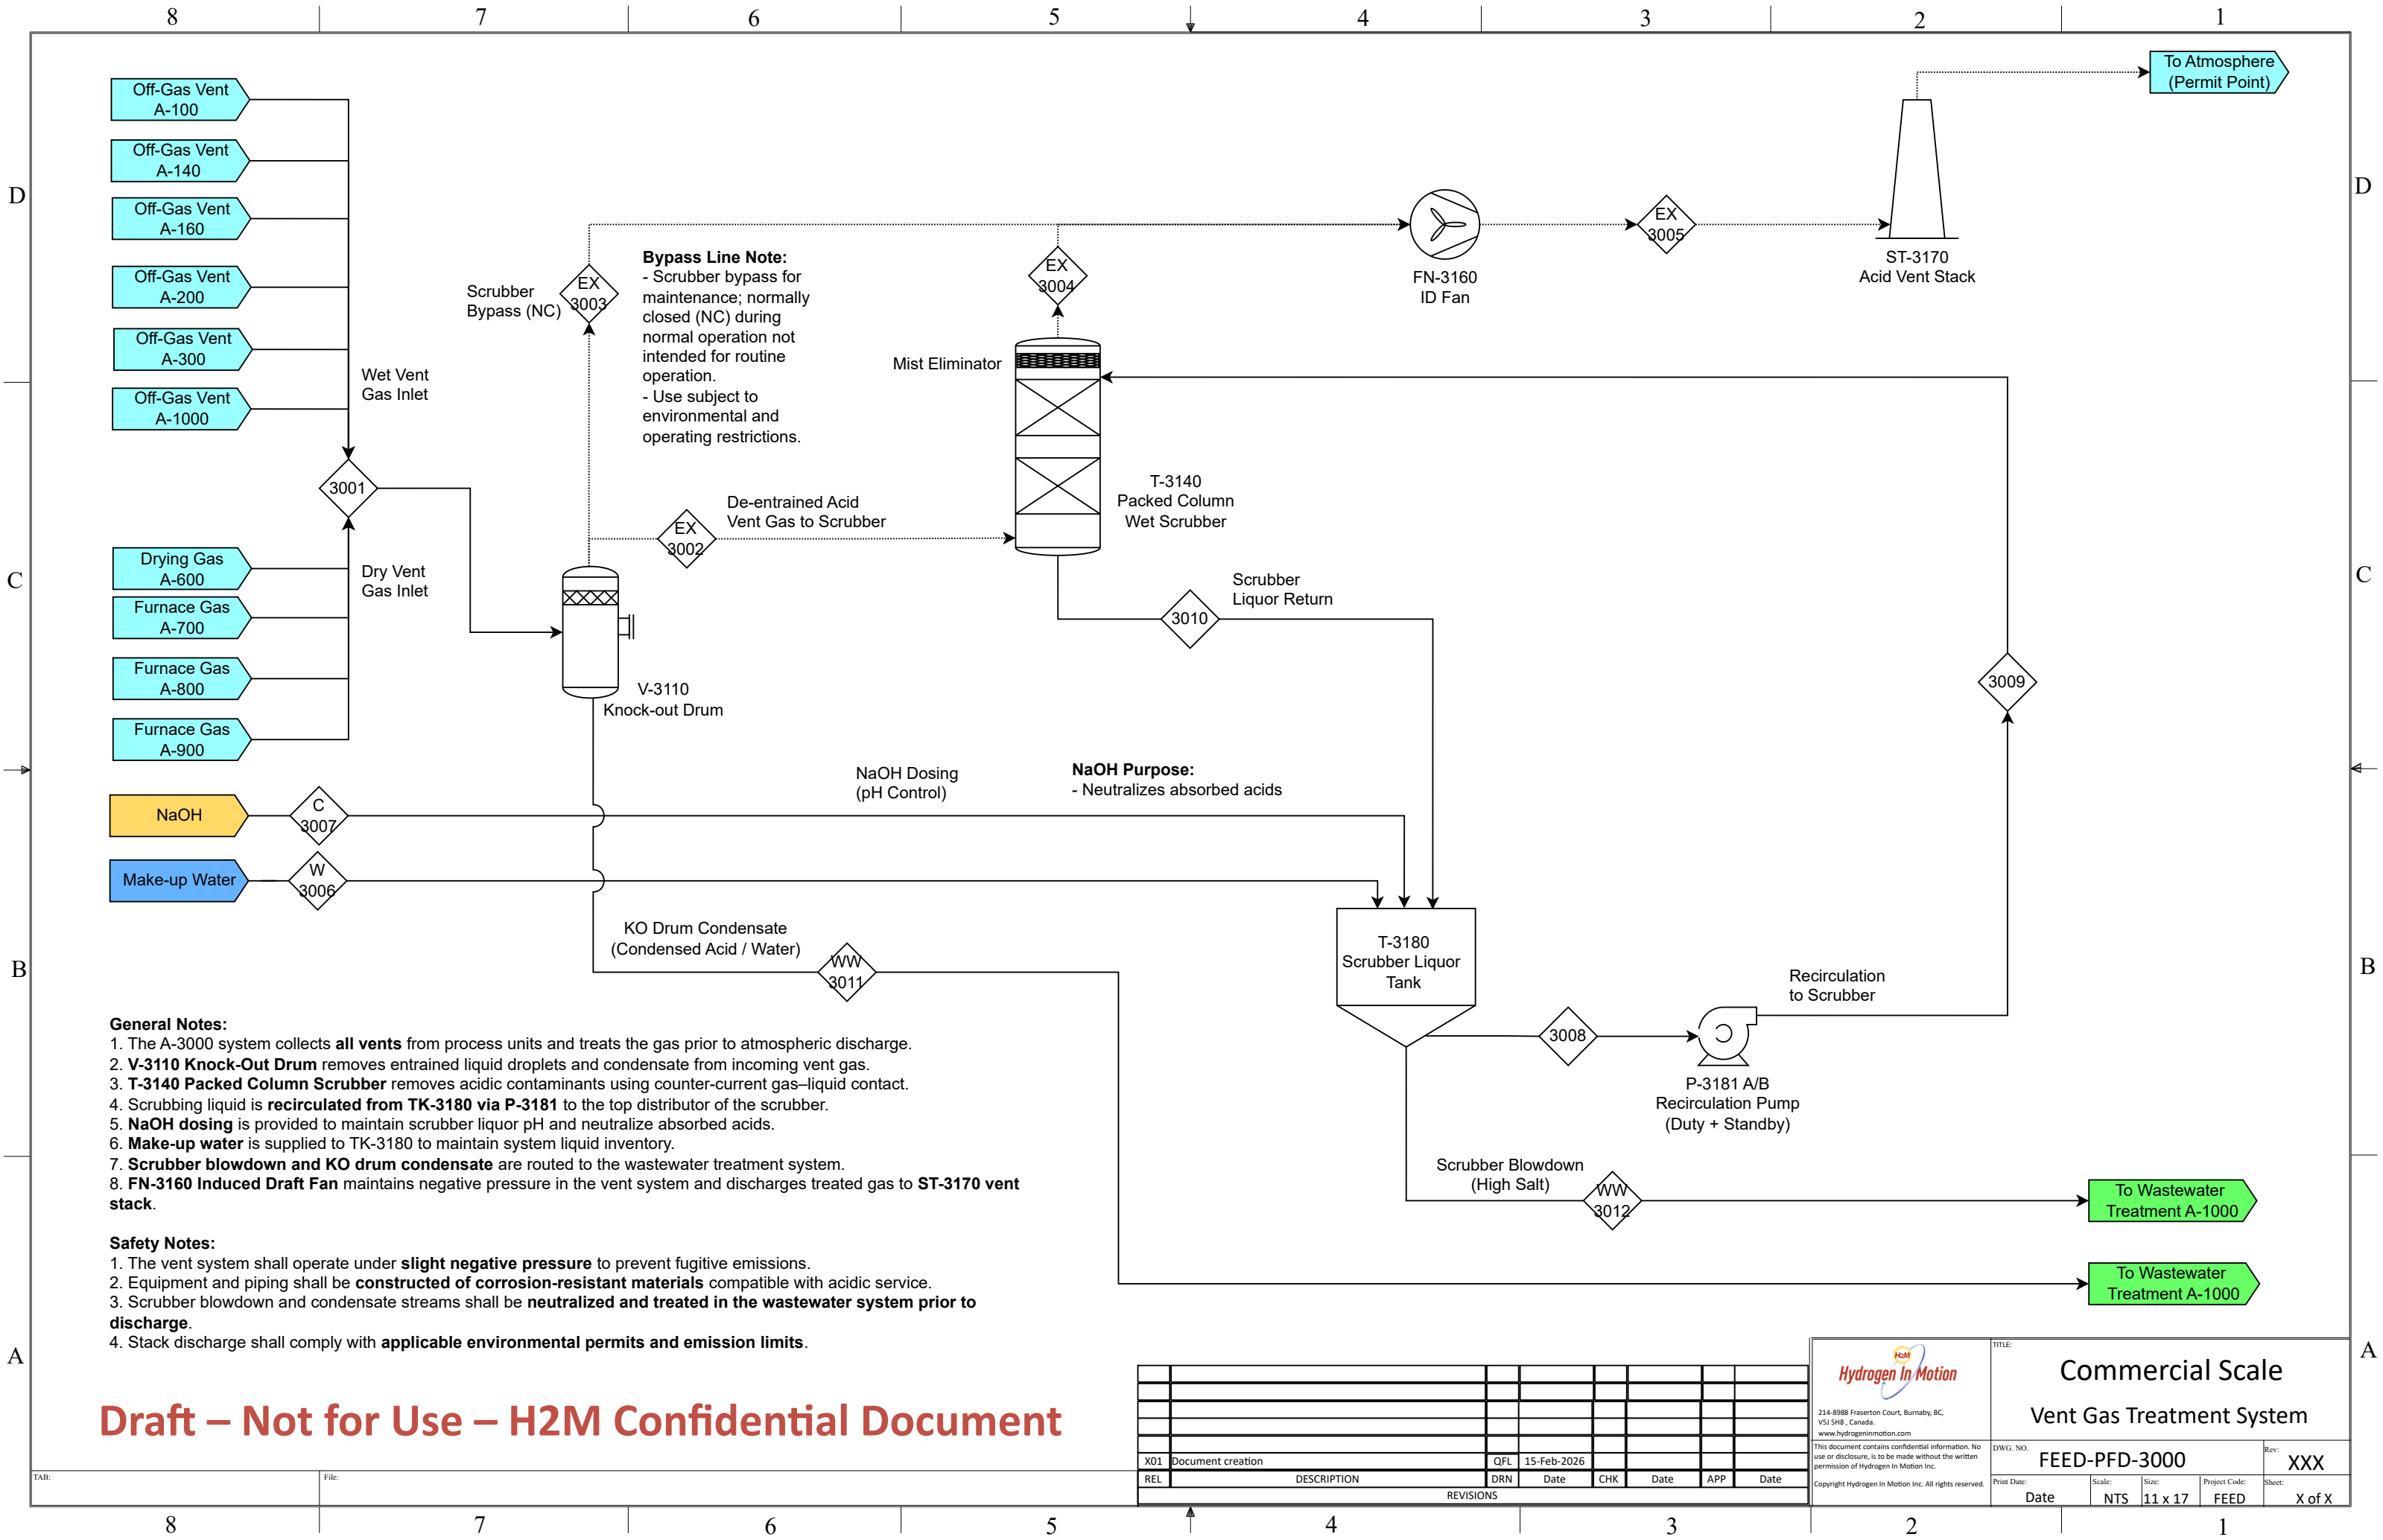

General Notes:

- 1. The A-3000 system collects **all vents** from process units and treats the gas prior to atmospheric discharge.
- 2. **V-3110 Knock-Out Drum** removes entrained liquid droplets and condensate from incoming vent gas.
- 3. **T-3140 Packed Column Scrubber** removes acidic contaminants using counter-current gas-liquid contact.
- 4. Scrubbing liquid is **recirculated from TK-3180 via P-3181** to the top distributor of the scrubber.
- 5. **NaOH dosing** is provided to maintain scrubber liquor pH and neutralize absorbed acids.
- 6. **Make-up water** is supplied to TK-3180 to maintain system liquid inventory.
- 7. **Scrubber blowdown and KO drum condensate** are routed to the wastewater treatment system.
- 8. **FN-3160 Induced Draft Fan** maintains negative pressure in the vent system and discharges treated gas to **ST-3170 vent stack**.

Safety Notes:

- 1. The vent system shall operate under **slight negative pressure** to prevent fugitive emissions.
- 2. Equipment and piping shall be **constructed of corrosion-resistant materials** compatible with acidic service.
- 3. Scrubber blowdown and condensate streams shall be **neutralized and treated in the wastewater system prior to discharge**.
- 4. Stack discharge shall comply with **applicable environmental permits and emission limits**.

Draft – Not for Use – H2M Confidential Document

REVISIONS						
REL	DESCRIPTION	DRN	Date	CHK	Date	APP
X01	Document creation	QFL	15-Feb-2026			

		214-8988 Fraserston Court, Burnaby, BC, V5J 5H8, Canada. www.hydrogeninmotion.com		This document contains confidential information. No use or disclosure, is to be made without the written permission of Hydrogen In Motion Inc.	
TITLE:		Commercial Scale		DWG. NO.	
		Vent Gas Treatment System		FEED-PFD-3000	
Print Date:		Scale:		Size:	
Date		NTS		11 x 17	
Project Code:		FEED		Sheet:	
				X of X	