


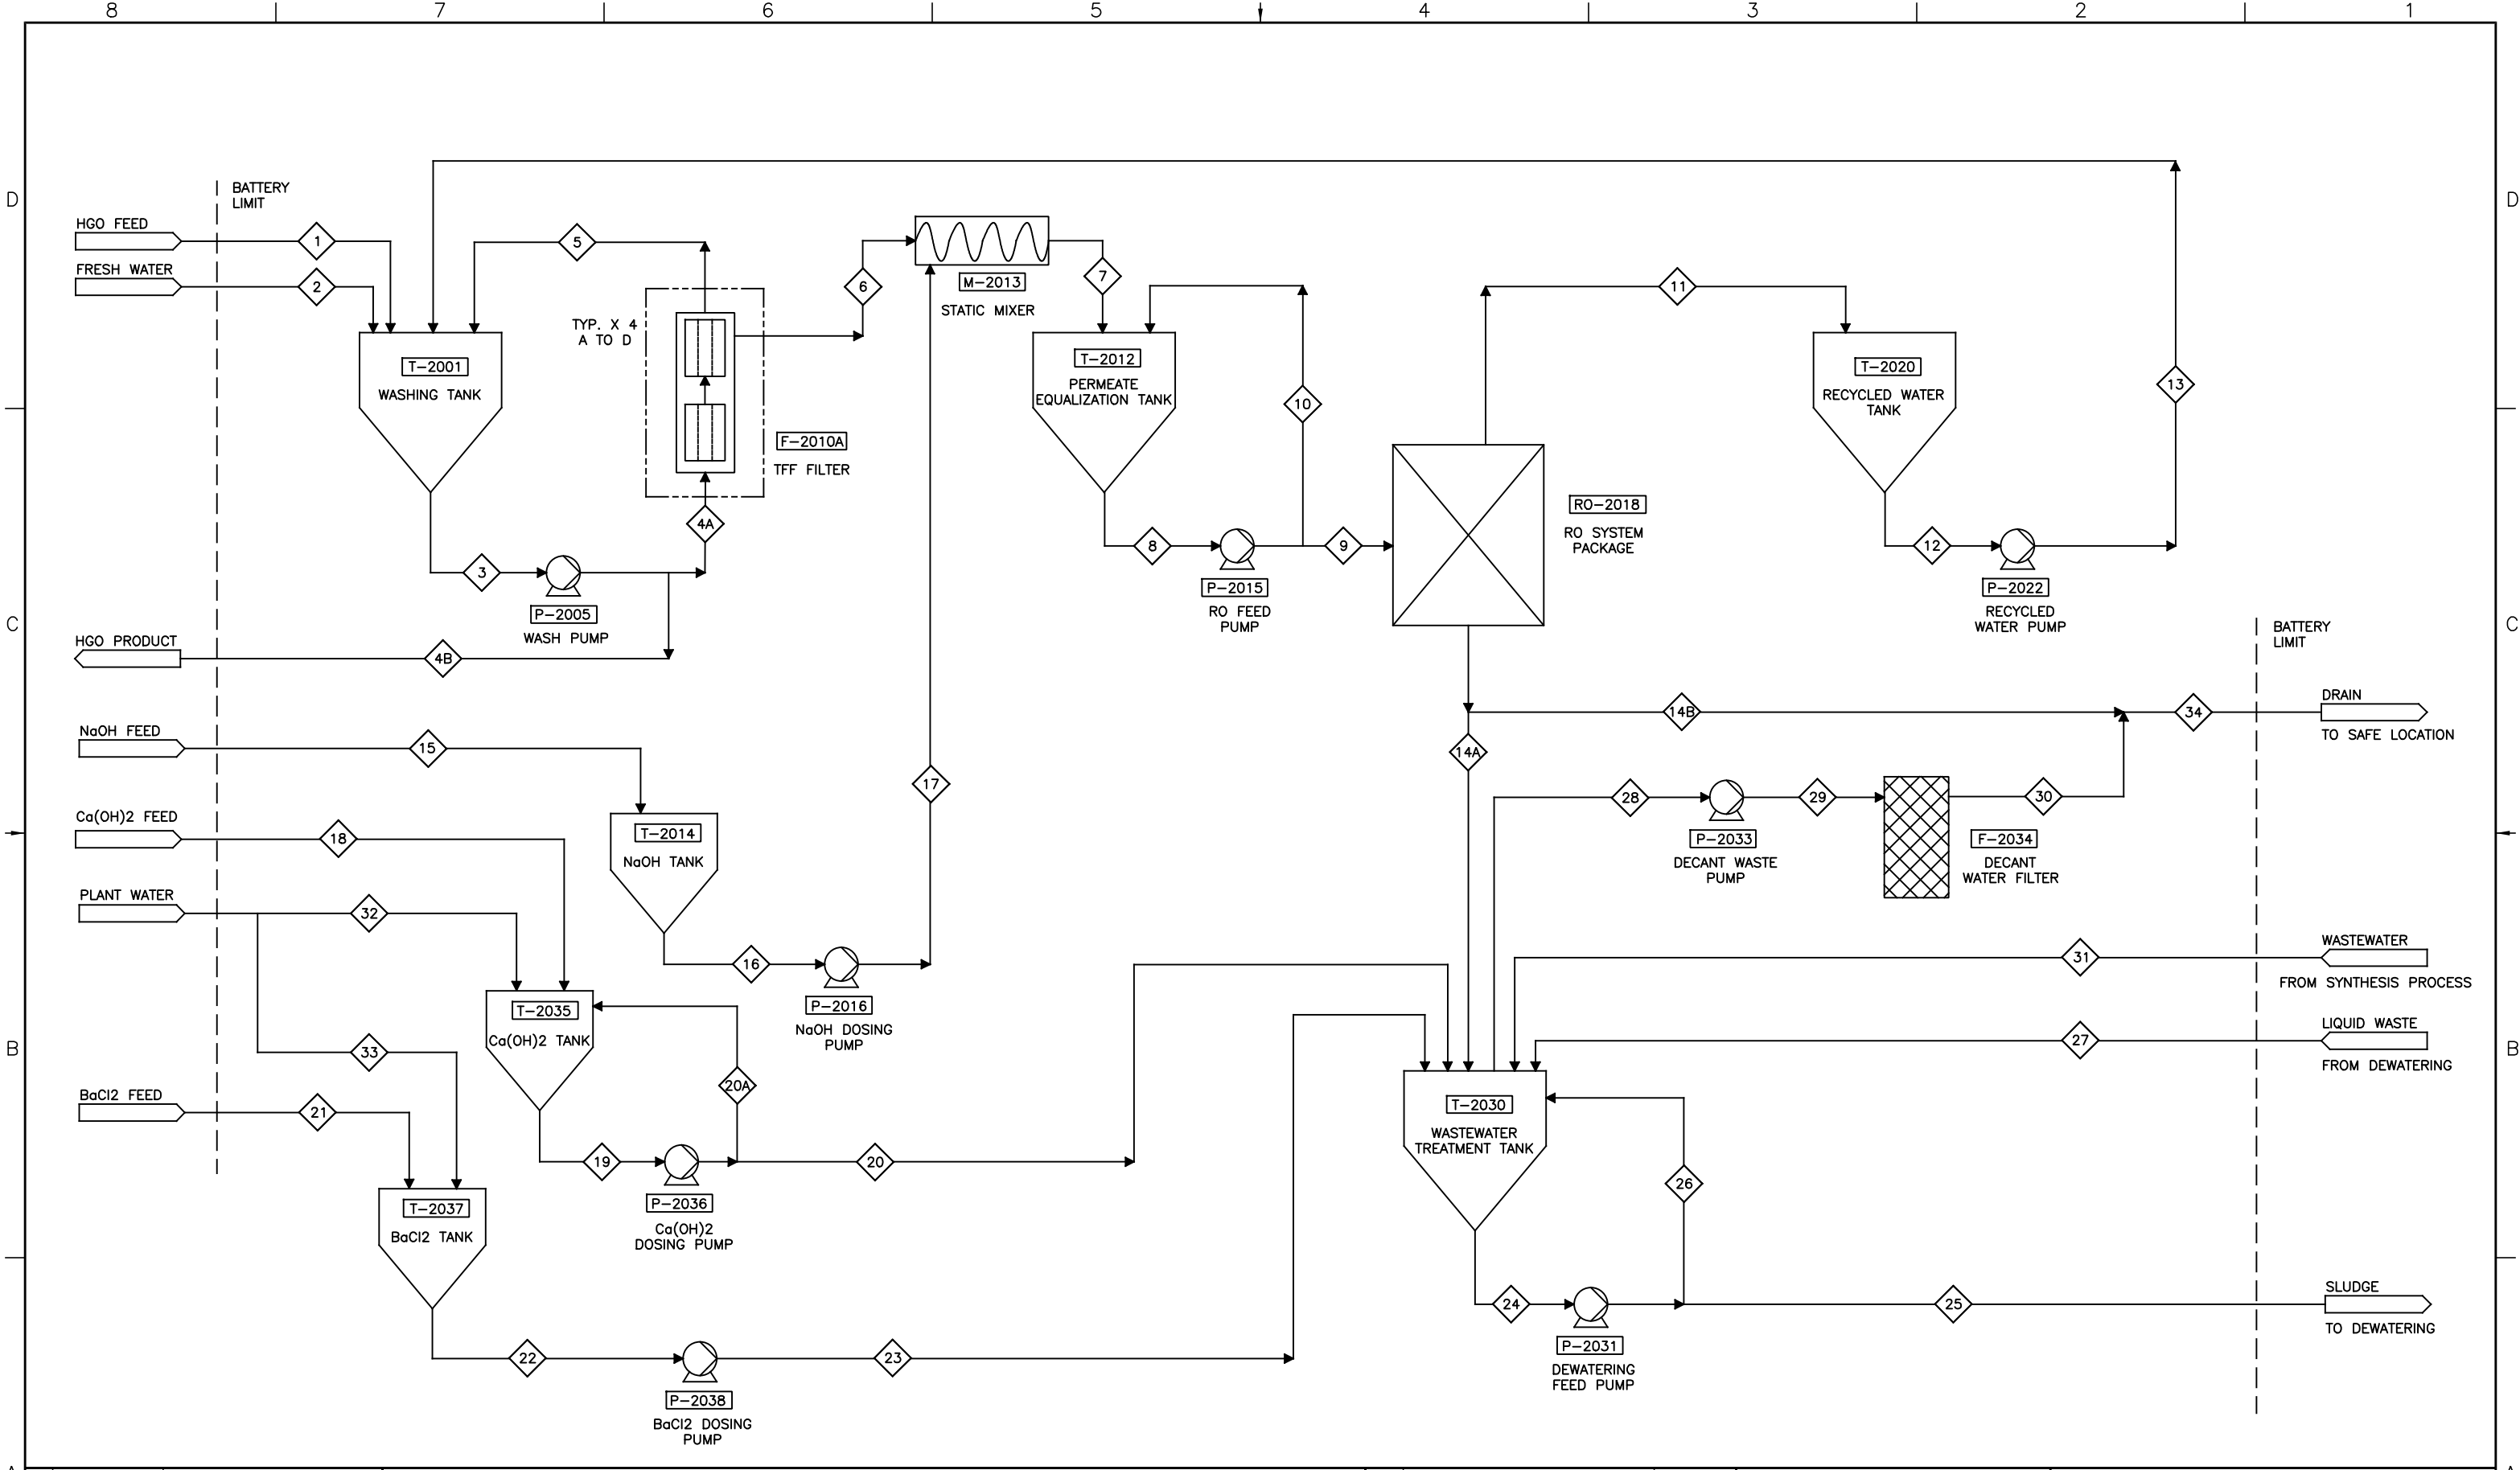

REFERENCE DRAWINGS	DRAWING NO.	DRAWING TITLE	NOTES:	REV	REVISION DESCRIPTION	DATE	 THIS DRAWING AND THE INFORMATION CONTAINED HEREIN IS CONFIDENTIAL, AND HAS BEEN PREPARED FOR HYDROGEN IN MOTION AND SHALL NOT BE COPIED, SUMMARIZED, LENT, DISCLOSED TO OTHERS OR USED FOR ANY OTHER PURPOSE OR RELIED UPON BY OTHERS WITHOUT THE PRIOR WRITTEN CONSENT OF AGEIAS ENGINEERED SYSTEMS LTD. ©2024 AGEIAS Engineered Systems Ltd.	 ENGINEERED SYSTEMS LTD.							
				A	PRELIMINARY – FOR CLIENT REVIEW	2024.06.10		DESIGNED			PROCESS FLOW DIAGRAM – WASHING SYSTEM PILOT PLANT	SIZE B	DWG NO. 1054ENG1–DWG–1001	REV A	
								DRAWN	TL	2024.06					
								CHECKED	AG	2024.06					
								APPROVED	AG	2024.06					
									NAME	DATE		SCALE	NTS	SHEET 1	OF 1

8

7

6

5

4

3

2

1